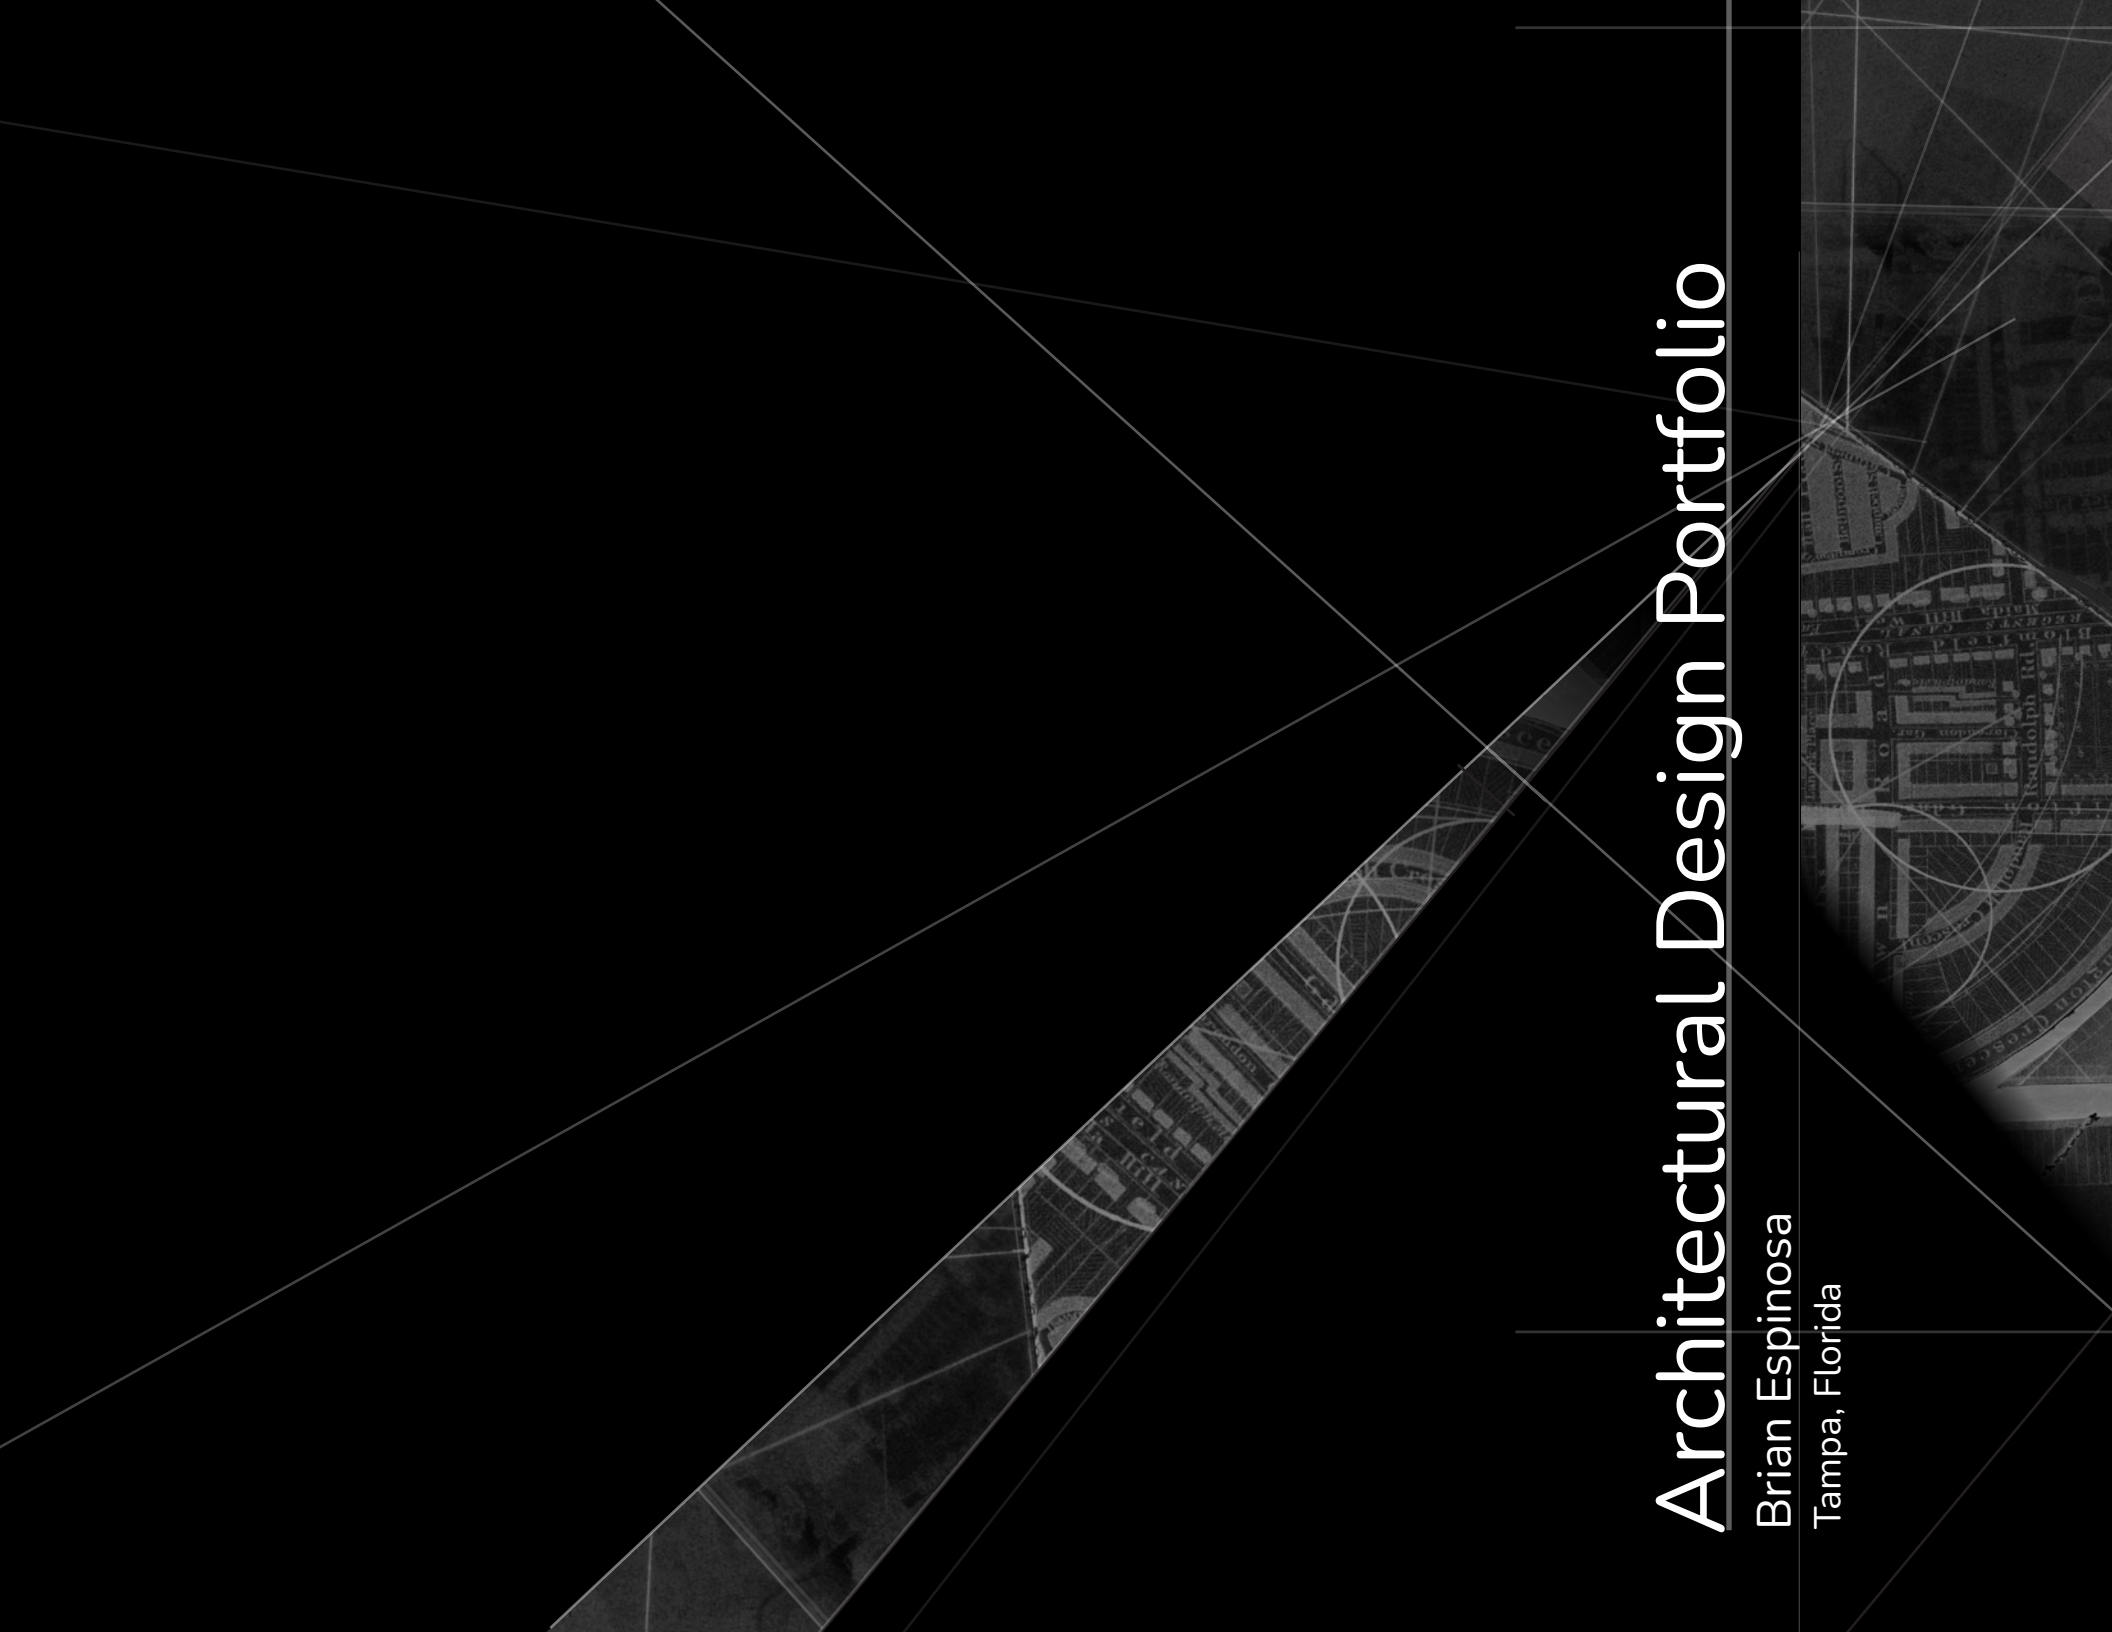


The background of the entire page is a dark, monochromatic architectural drawing. It features a complex network of thin, light-colored lines that intersect to form various geometric shapes, including triangles and polygons. Overlaid on these lines are several circular and semi-circular arcs, some of which are centered on specific points. In the lower right corner, there is a detailed, grayscale aerial photograph of a city grid, showing streets, buildings, and parks. The overall aesthetic is technical and precise, typical of architectural or engineering design.

# Architectural Design Portfolio

Brian Espinosa

Tampa, Florida

|   |                         |  |   |               |
|---|-------------------------|--|---|---------------|
| I | S C H A R H S           |  | Location: Tampa, Florida<br>2023 - Present (Formally Known as Zyscovich)<br>Field of Work: Education<br>Project Coordinator | Pages 01 - 02 |
|   | I H - Σ S Σ A I S M R G |  | Location: Tampa, Florida<br>2021 - 2023<br>Field of Work: Commercial<br>Project Coordinator                                 | Pages 03 - 04 |

|                         |  |                                                         |                              |
|-------------------------|--|---------------------------------------------------------|------------------------------|
| Γ A Z O - S S M T O R P |  | Stratus (Formally Known as Zyscovich)<br>2023 - Present | Gresham Smith<br>2021 - 2023 |
|-------------------------|--|---------------------------------------------------------|------------------------------|

|                   |  |   |                                                                                |
|-------------------|--|---|--------------------------------------------------------------------------------|
| C - Σ M D A C A   |  | Undergraduate: University of Florida (2018 - 2021)<br>Bachelor of Arts Design: Architecture            | Graduate: University of South Florida (2022 - 2024)<br>Masters of Architecture |
| M H A < - H Γ C C |  | Location: Chelsea, New York<br>Architectural Design Class: Fall 2020 (UF)<br>Instructor: Alfonso Perez | Pages 05 - 08                                                                  |

|               |  |   |               |
|---------------|--|---|---------------|
| Γ A M C Z O C |  | Location: San Juan, Puerto Rico<br>Architectural Design Class: Spring 2023 (USF)<br>Instructor: Steve Cooke | Pages 09 - 12 |
|---------------|--|---|---------------|

|                   |  |   |               |
|-------------------|--|---|---------------|
| M H A R H M Z M P |  | Location: Mann-Wagon Memorial Park Tampa, Florida<br>Architectural Design Class: Spring 2023 (USF)<br>Instructor: Steve Cooke | Pages 13 - 14 |
|-------------------|--|---|---------------|

|                     |  |   |               |
|---------------------|--|---|---------------|
| M H A R O G - < Z - |  | Location: Palm Point Park, Gainesville Florida<br>Architectural Design Class: Fall 2019 (UF)<br>Instructor: John Maze | Pages 15 - 16 |
|---------------------|--|---|---------------|



# 2021 – Current Professional Works

Construction is phased so that students can continue learning on-site while the new facility is built. Once the new building is completed, the existing structures will be demolished and the remaining site work—including parking and campus improvements—will be finalized. The project began construction in summer 2025 and is expected to be fully completed by 2027.



Exterior Render

The building is arranged in an L-shaped configuration to improve campus circulation and organize clear separation between student areas, bus circulation, and parent drop-off. A welcoming entry plaza establishes a civic presence for the school while expanding queuing capacity to reduce traffic congestion on adjacent roads.



Exterior Render



Interior Render

Gulf Middle School is a comprehensive campus redevelopment currently under construction in New Port Richey, Florida. The project replaces the existing aging facilities with a modern educational environment designed to support contemporary teaching methods while allowing the school to remain operational throughout construction.

## Stratus

Gulf Middle School  
New Port Richey, Florida



Exterior Render



First Floor Plan

Future high school students in Wellen Park will study science in an outdoor living lab, collaborate on project-based assignments in a large common areas, enjoy a collegiate-inspired student union and get a jump start on skills needed by local companies.

With nature as its guide, the 2,100-person capacity student building represents the future of Sarasota high schools. The \$175 million high school — the first built by Sarasota County Schools in 30 years — is located on River Road and the future Manasota Beach Road extension. Expected to open in August 2025, the 325,000-square-foot school is a radical departure from traditional sprawling campuses. The compact three-story design improves security and student circulation, Jane Dreger, director of construction services, told the school board.

The single-building Wellen Park facility will feature signature spaces including a welcome center designed to encourage parent participation; a common areas functioning as a cafeteria, the school's largest classroom and a community event space; an innovation zone housing engineering, entrepreneurial and tourism labs; the second-floor student union with a library, counseling and career services overlooking the commons area; an 850- seat performing arts center; and a championship gymnasium with training and athletic centers.

The high school is one of three new schools planned for more than 4,200 students in the rapidly growing Wellen Park, ranked the second-fastest growing community in the country for 2022. Also coming is a for-profit K-6 charter school — for more than 600 students, expected to open this fall — and Sarasota County Schools' planned K-8 school next to the new high school.

Wellen Park is planned for 22,500 homes and 50,000 residents — more than five times its current population of about 9,500 residents.



Exterior Render



Interior Render



Exterior Render





Exterior Render

Parking will be conveniently located underground and out of site, while designated on-street ride-sharing drop-off and pick-up areas will be provided.



Exterior Render




Exterior Render

# Gresham Smith

## Nashville Yards Parcel 9 Nashville, Tennessee

When real estate investors Southwest Value Partners purchased a 16-acre site in a prime location on the western edge of downtown Nashville, Gresham Smith was brought on to help reimagine its potential. The result is a high-quality, urban community that celebrates Nashville's roots while introducing an eclectic mix of spaces that continues to advance the world-class city.

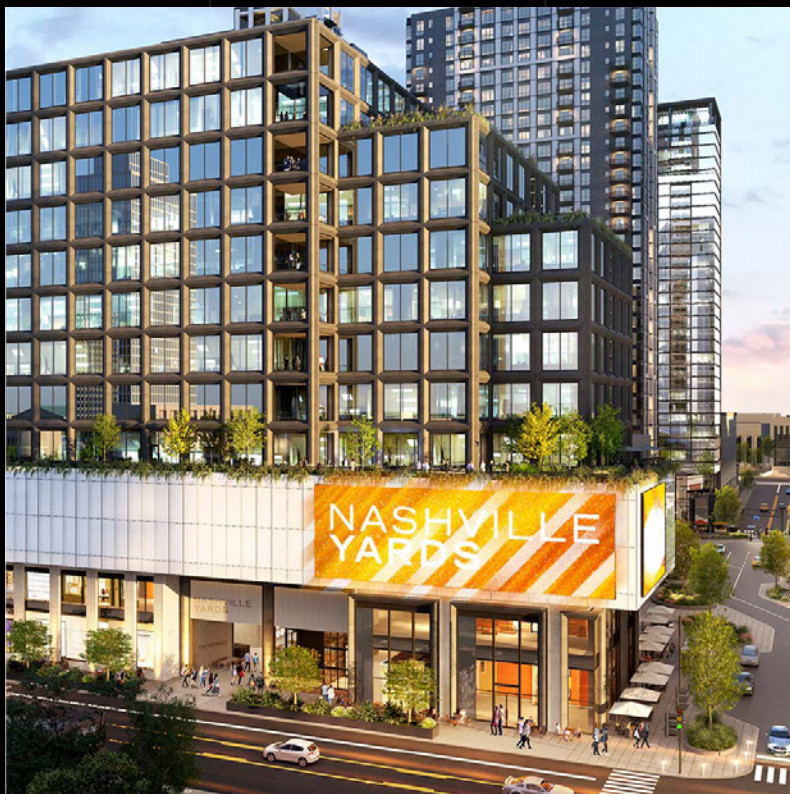

Exterior Render



Exterior Render

Nashville Yards site was once a railyard: the place that people and goods entered Nashville. With the new development, Nashville Yards once again becomes the gateway to the city through the creative combination of additions to the city's skyline and a layered walkable environment.



Exterior Render

Integrated design features such as pedestrian plazas and common branding elements that influence the way people will engage with streets, sidewalks and lighting will create a holistic feeling within Nashville Yards.



Exterior Render

Overall, the project is estimated to generate over \$36 billion in economic impact to the region.



Exterior Render



River Walk Render

Gresham Smith and DLR group joined to create the Straz Center expansion project by adding new functions and activities.

The expansion of the complex resolves several key challenges restricting Straz's ability to remain a state-of-the-art performance facility.



Interior Render

Straz will also be adding a series of interventions such as an expanded lobby, updated food and beverage services, a new event center, an arrival plaza, and outdoor event terraces.



Exterior Render

These new interventions will provide additional opportunities for revenue generation and reinforce the experience of the Straz Center.

# Gresham Smith

## Straz Performing Arts Center Tampa, Florida

The David A. Straz Center for the Performing Arts commands a prominent 10-acre site along the Hillsborough River, and is the sixth largest performing arts center in the U.S. Built in 1987 on an abandoned gravel lot, it is now home to Opera Tampa, the Patel Conservatory, and six theaters/rehearsal halls.



Interior Render

The Straz expansion will contain a redesigned vehicular road system which provides much-needed space for parking and simplifies pedestrian and vehicular circulation. These upgraded roads will enhance the connection of the Straz to the river and downtown core.



Exterior Render



Exterior Render




Exterior Render




Techniques:  
AutoCAD  
Lumion  
Photoshop  
RayTrace  
Rhino

Traditional farming will no longer satisfy the growing population of New York and will need to be supplemented and replaced. Vertical farming would be introduced into the site to **enrich** the population with fresh produce.

The experimental and artistic nature of Chelsea, New York provides an ideal location for a new agricultural program that introduces new technology into a dense fabric, thus re-defining agriculture in a city.

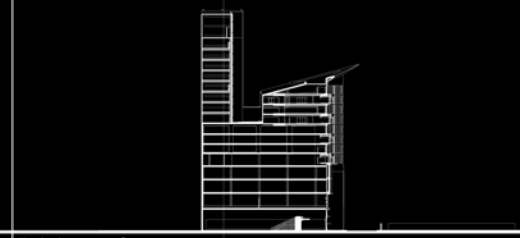

Exhibition Section

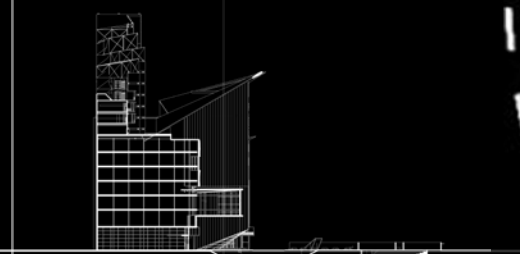


Library Section




Vertical Farm Section



Chelsea park is considered one of the busiest public spaces in the neighborhood. The existing park was designed for the community with many visitors that vary from **passive** to **active** recreation.

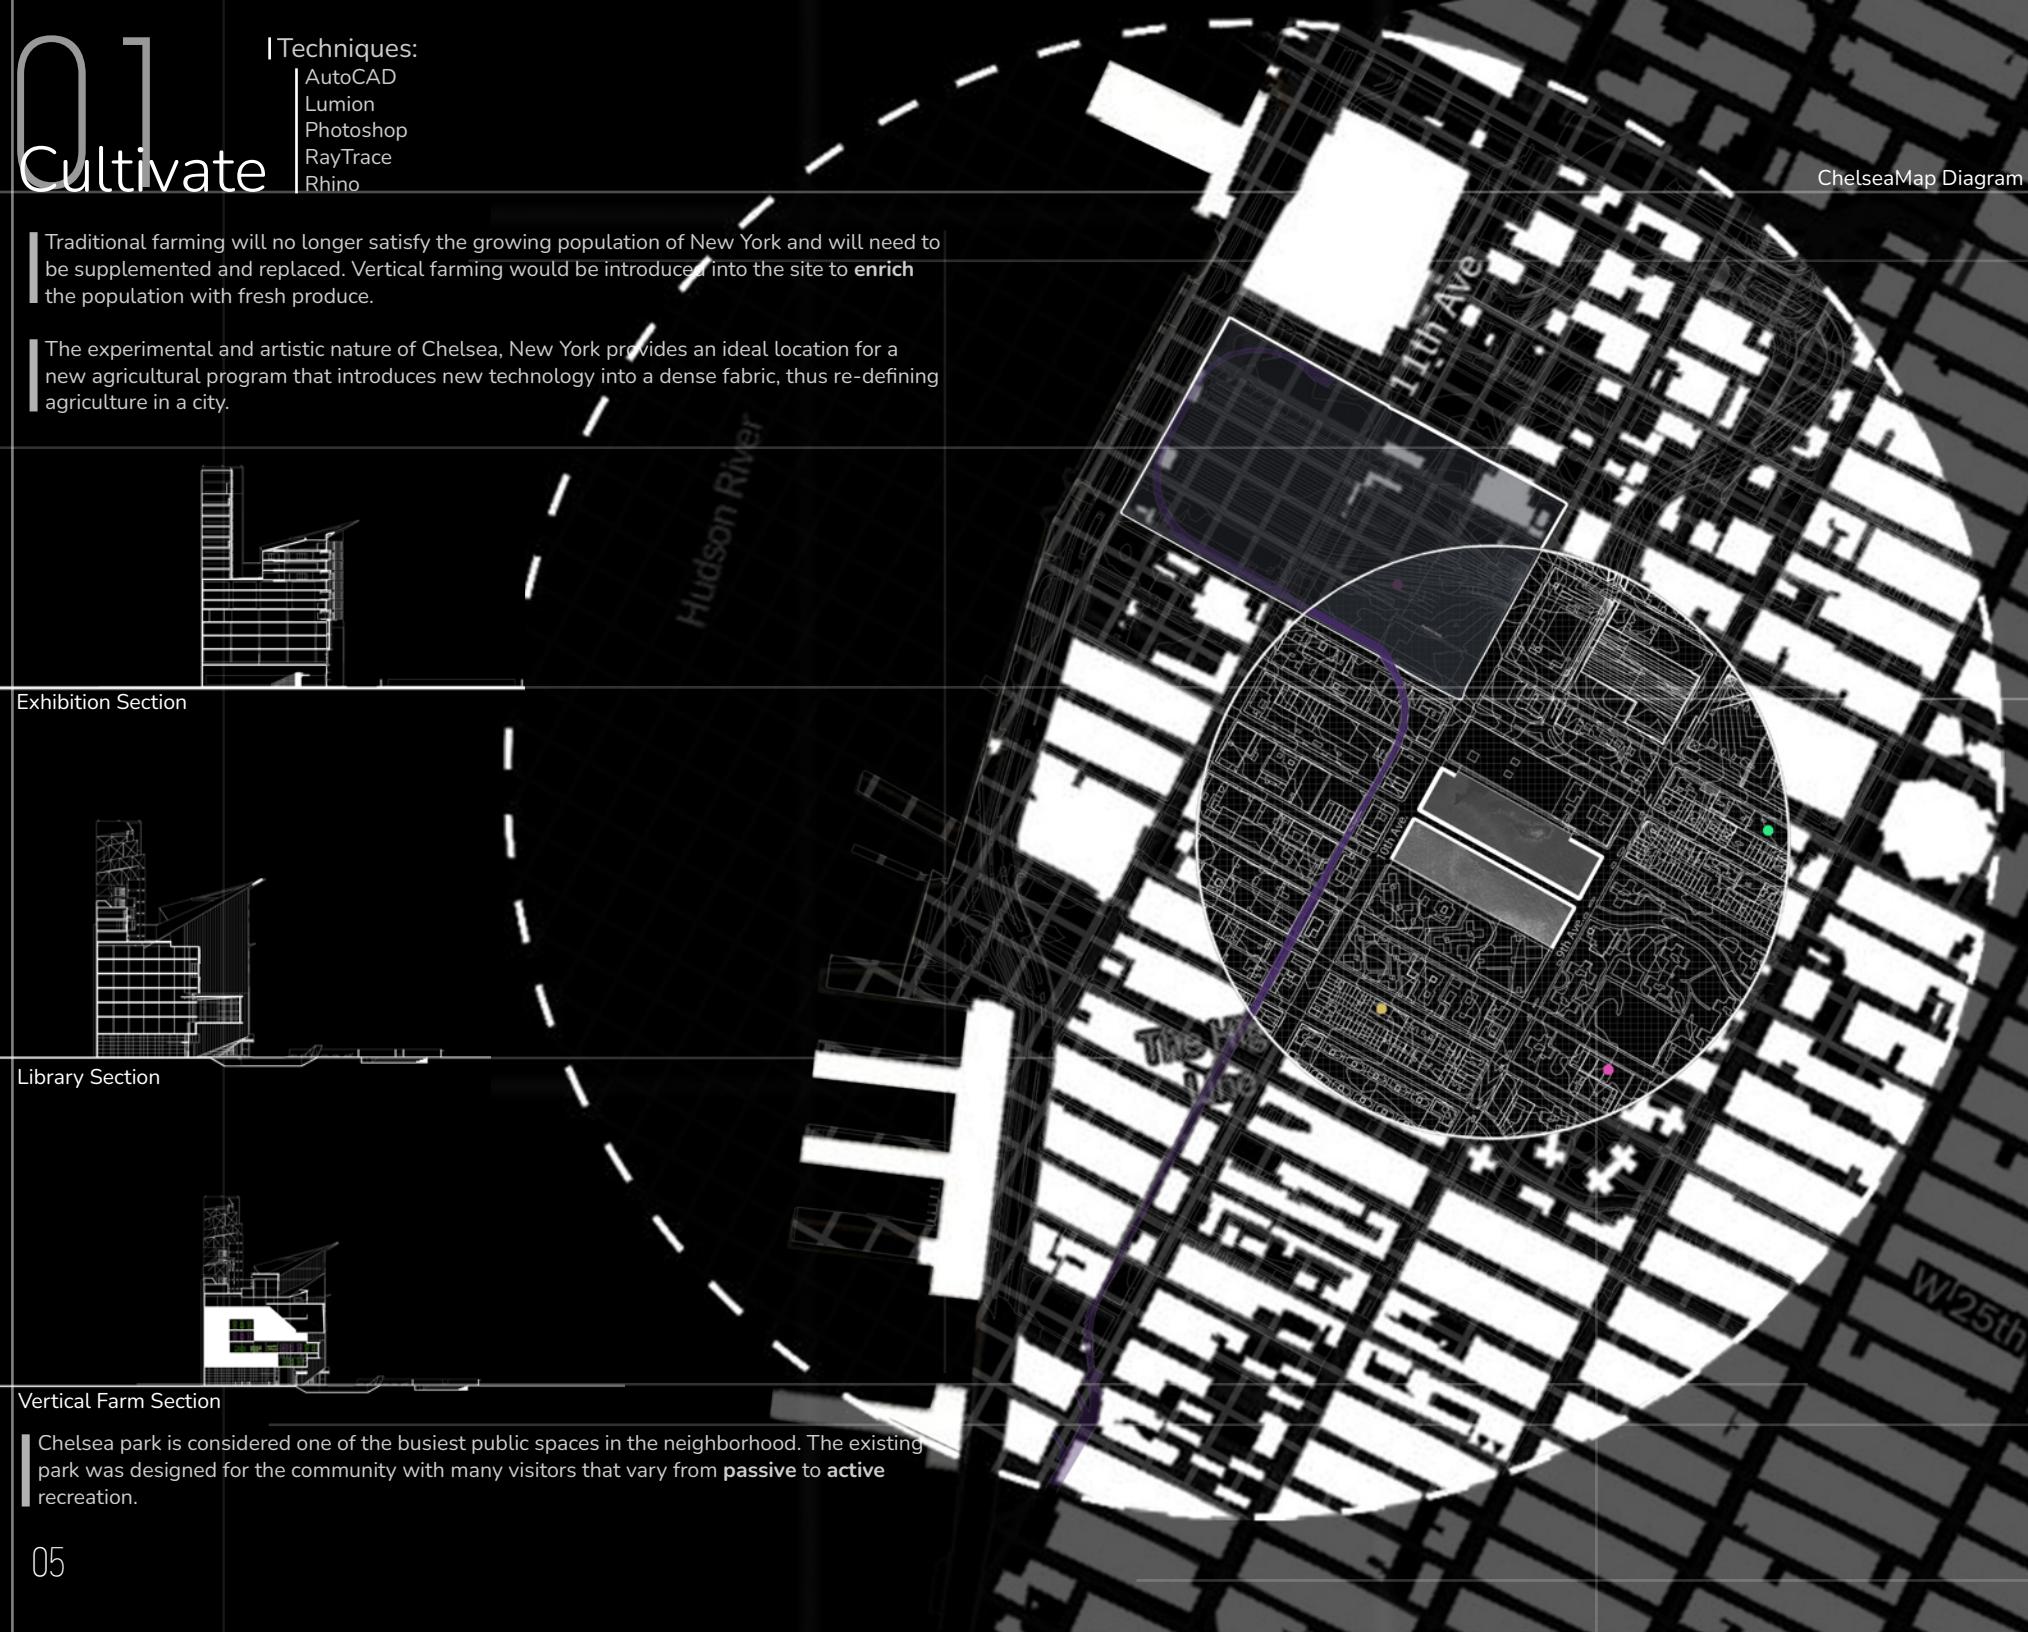

ChelseaMap Diagram

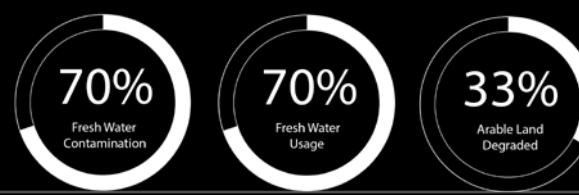

## Environmental Effects of Traditional Agriculture

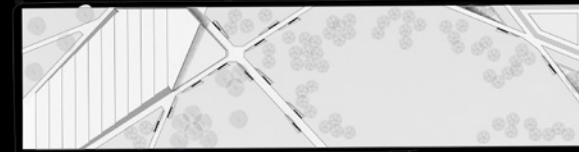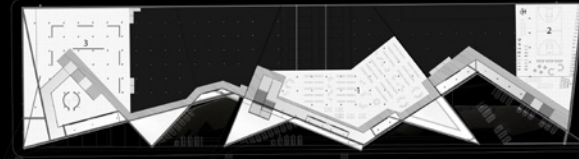


As dense living becomes an undeniable reality, field farming will become less and less relevant as cities expand into rural areas. Traditional farming will no longer be able to satisfy the growing populations.

The Cultivate Project introduces **controlled environment farming** to the Chelsea neighborhood. The high-density nature of this type of agriculture uses 95% less water than field agriculture and allows for the water to be recycled.

The form is inspired by an **abstracted form** of the standard New York City block. The architecture of the modularity of brownstones was pulled and pushed by creating edges into the jagged structures on the 28th street Façade. In a city where relaxed public outdoor space is highly coveted, this form allows for smaller pockets of relaxed space in a public setting.

First Floor Plan with Context

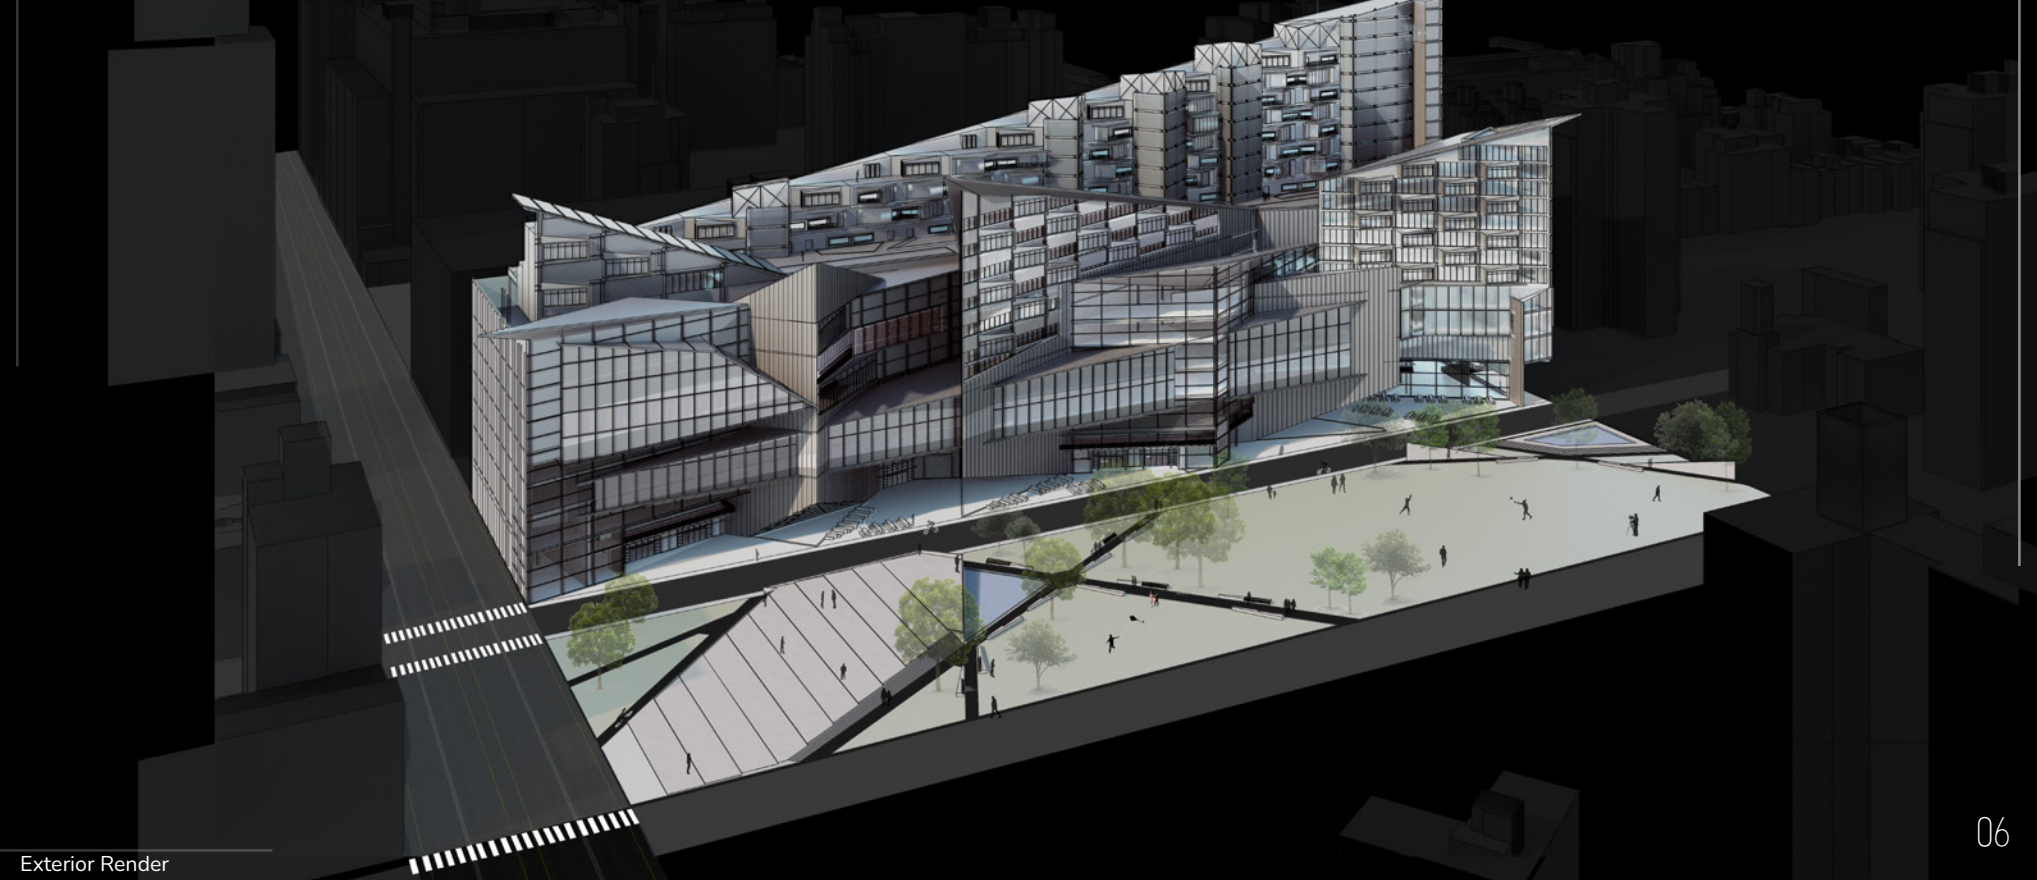


Exterior Render



Interior Library Perspective



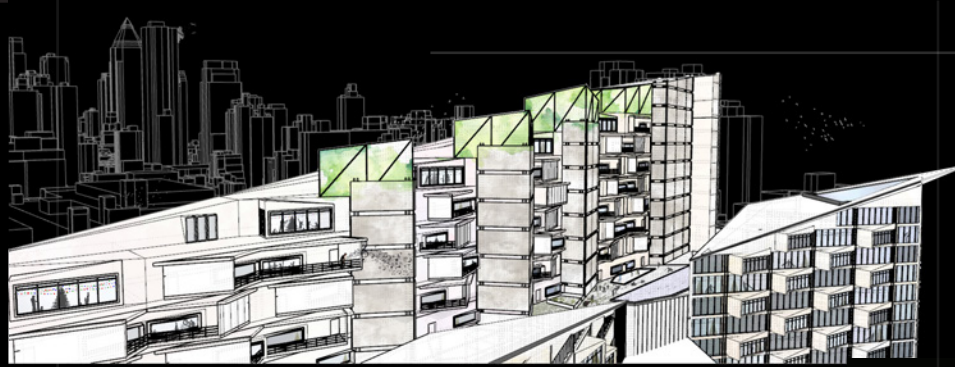

Exterior Apartment Perspective

The apartments in the project were designed to house two types of groups: **private** and **communal**.



Initial Design Sketch


The **private** group consists of the residential portion of the building and would cater towards the professional population. The **communal** group would house students attending the educational classes offered within the building.

The vertical farms offer a unique design that can grow plants in **high densities** with relatively low floor space use - an ideal program for food production in a city like New York City. Since vertical farming is sustained solely on artificial lighting, it is an **ideal program** for these problematic spaces.

Controlled environment farming is a newer method in the agricultural industry, and the **potential** has yet to be fully realized. Especially in the city of New York where the blocks are notoriously large and therefore contain substantial core spaces.

For a farming facility of this size, the addition of a body of students and researchers will be **invaluable** in the pursuit of further advancing the awareness and production of types of farming that are still being explored.

The library will specialize in environmental sciences to benefit the institute and educate the community on how to live **sustainably**. The students at the institute will have access to the farming facility to study, test, research, and develop technical **innovations** and push boundaries of biotech in controlled environments.

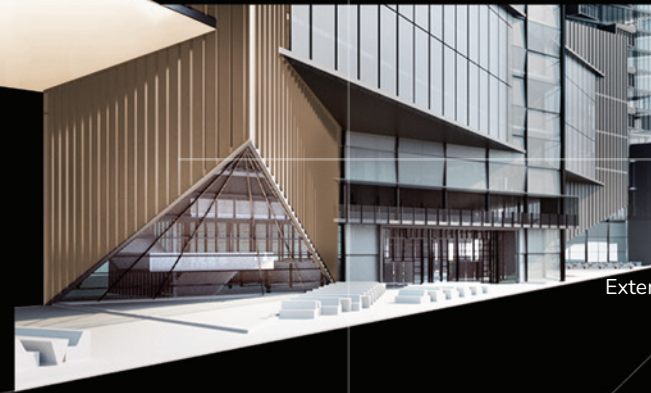

Exterior Render



Section Elevation

Project Cultivate is centered around **plant production** and **research**. It aims to cultivate the community and encourage **growth** in its community through **education**, access to better food choices, and awareness. In locations like New York City, there are always ways to live more sustainably.



Exterior Render



# 02 Conceal

Techniques:  
AutoCAD  
Hand Drawing  
Photography  
Physical Model Building  
Lumion  
Rhino

Project Conceal focuses on the location of a historic site with rich history. The site is located in Old San Juan, Puerto Rico. The site is situated next to the fort wall of San Juan that once defended off invaders and created protection for the people who inhabited San Juan many years ago.

The site contains **exquisite** views to the edge of the fort and the ocean beyond. The architecture was imperative not to interrupt the view that many tourists and locals travel to for entertainment.


By building underground, valuable surface land can be **preserved** for parks, gardens, recreational areas, and natural habitats. This approach helps **maintain green spaces** and contributes to the overall **quality of the urban environment**.



Interior Render



Exterior Render


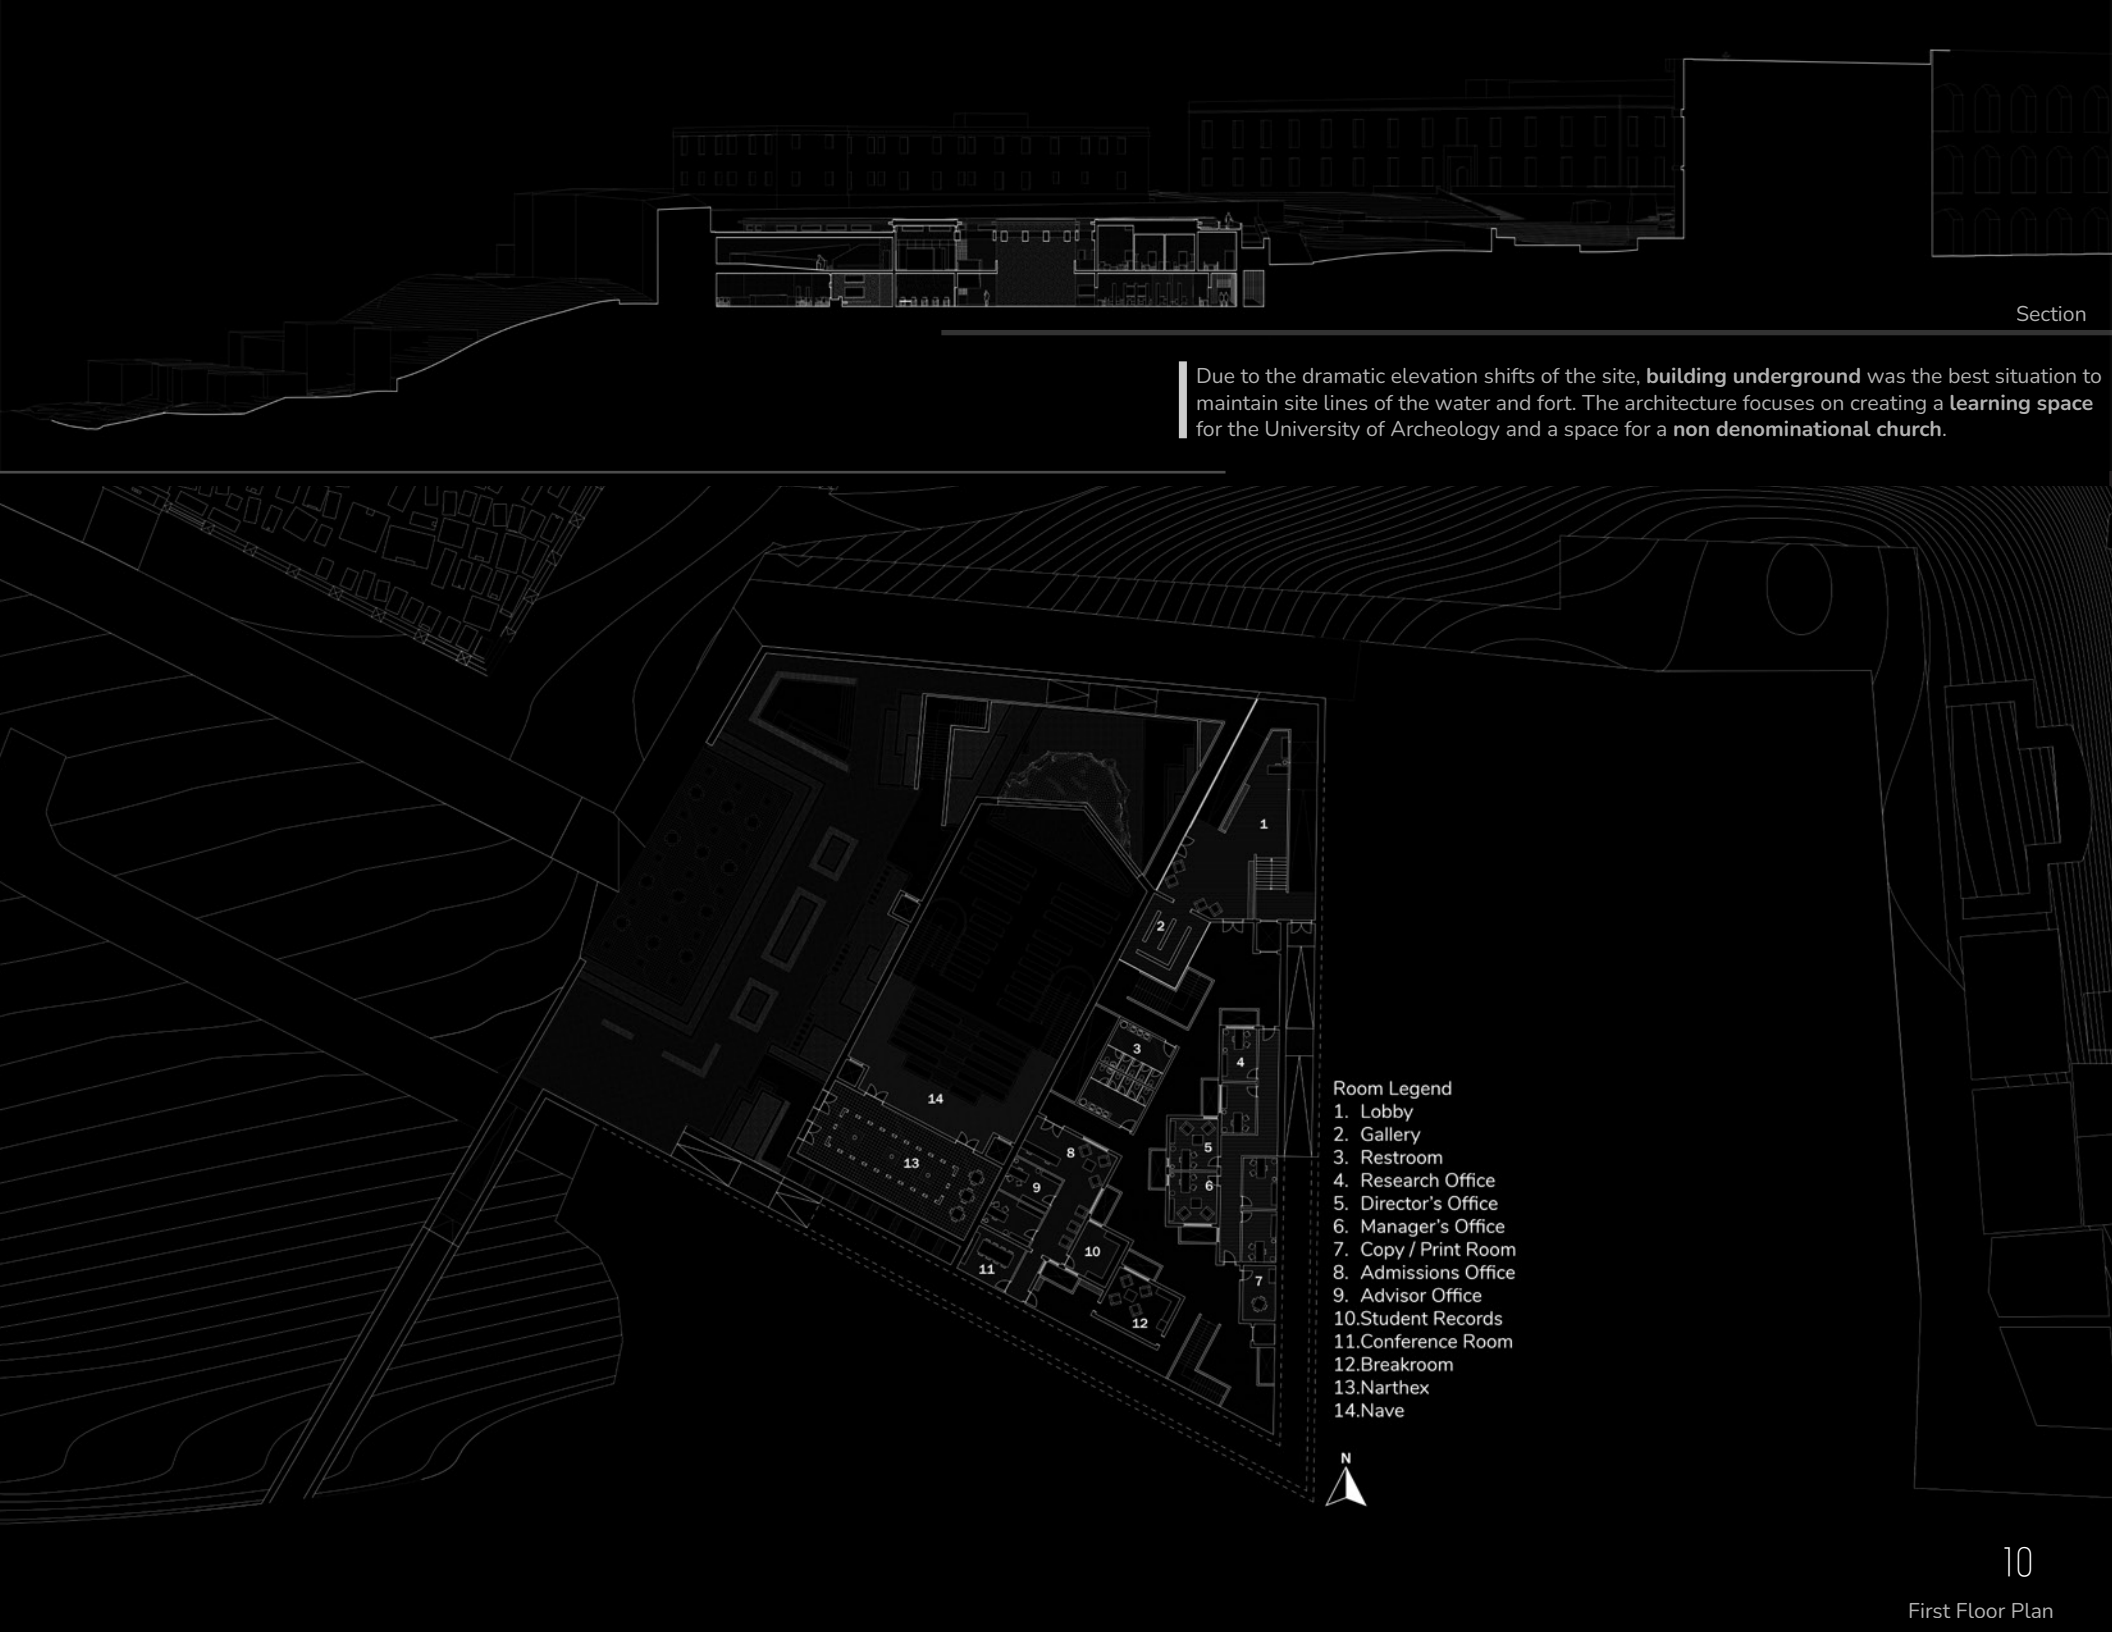


- Room Legend
- 1. Lobby
  - 2. Gallery
  - 3. Restroom
  - 4. Research Office
  - 5. Director's Office
  - 6. Manager's Office
  - 7. Copy / Print Room
  - 8. Admissions Office
  - 9. Advisor Office
  - 10. Student Records
  - 11. Conference Room
  - 12. Breakroom
  - 13. Narthex
  - 14. Nave

Section

Due to the dramatic elevation shifts of the site, **building underground** was the best situation to maintain site lines of the water and fort. The architecture focuses on creating a **learning space** for the University of Archeology and a space for a **non denominational church**.



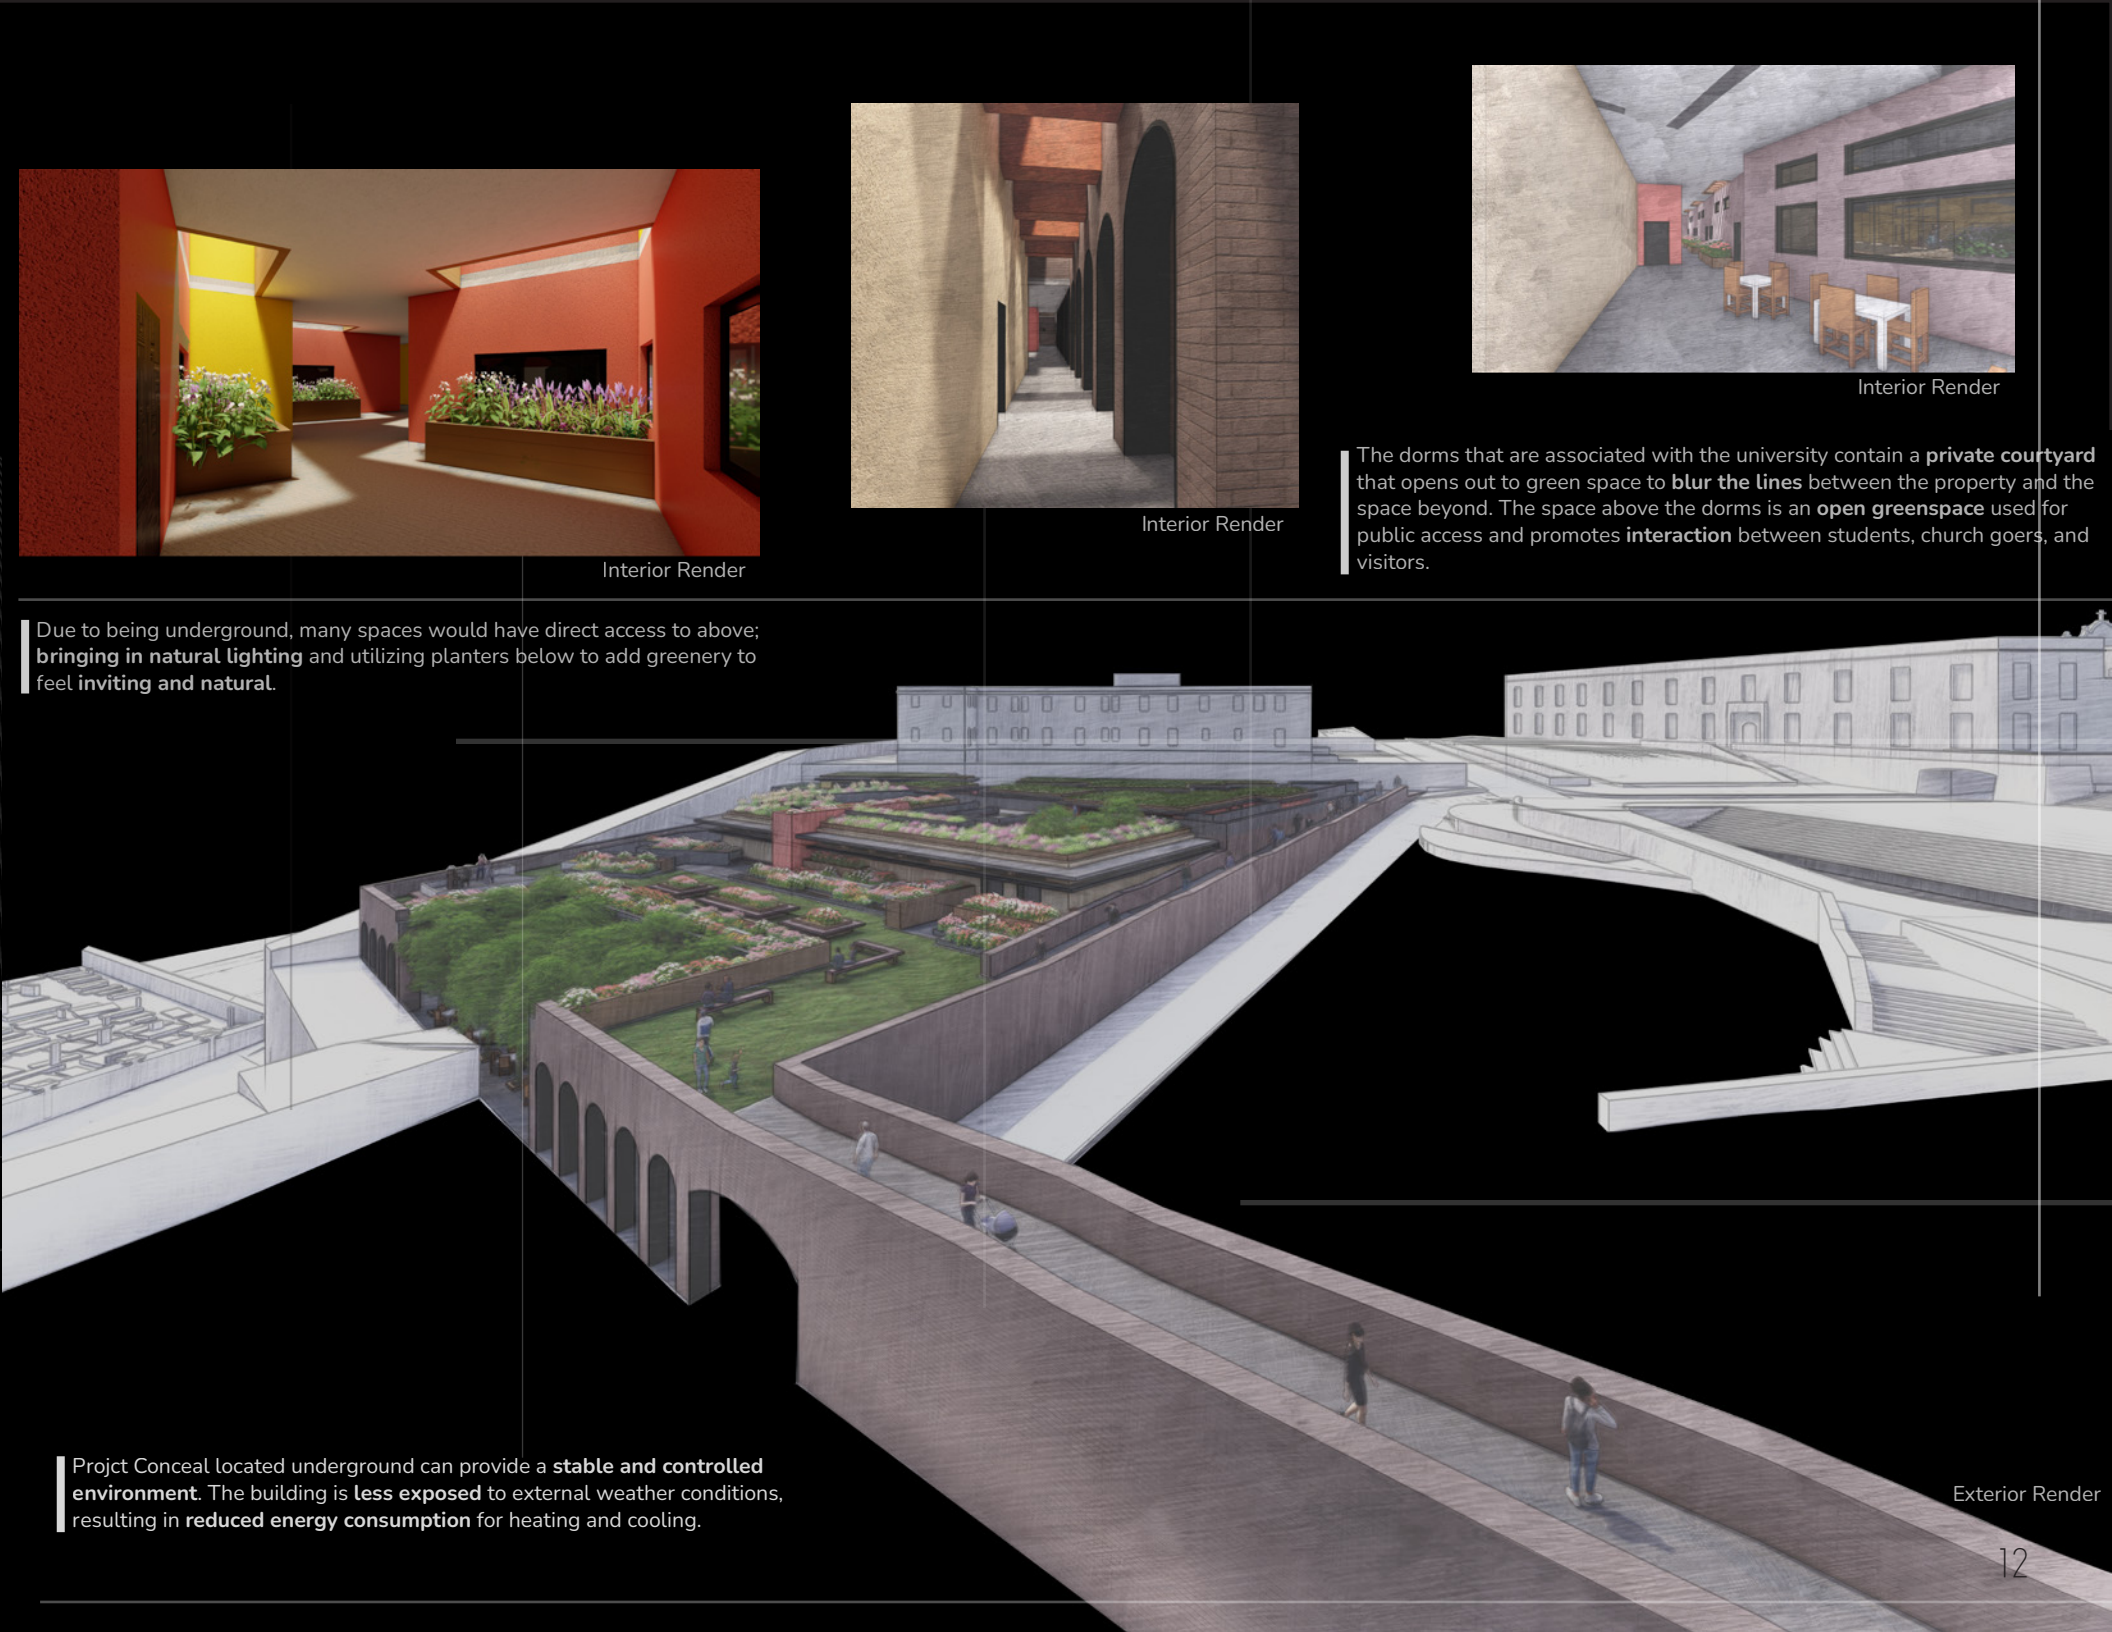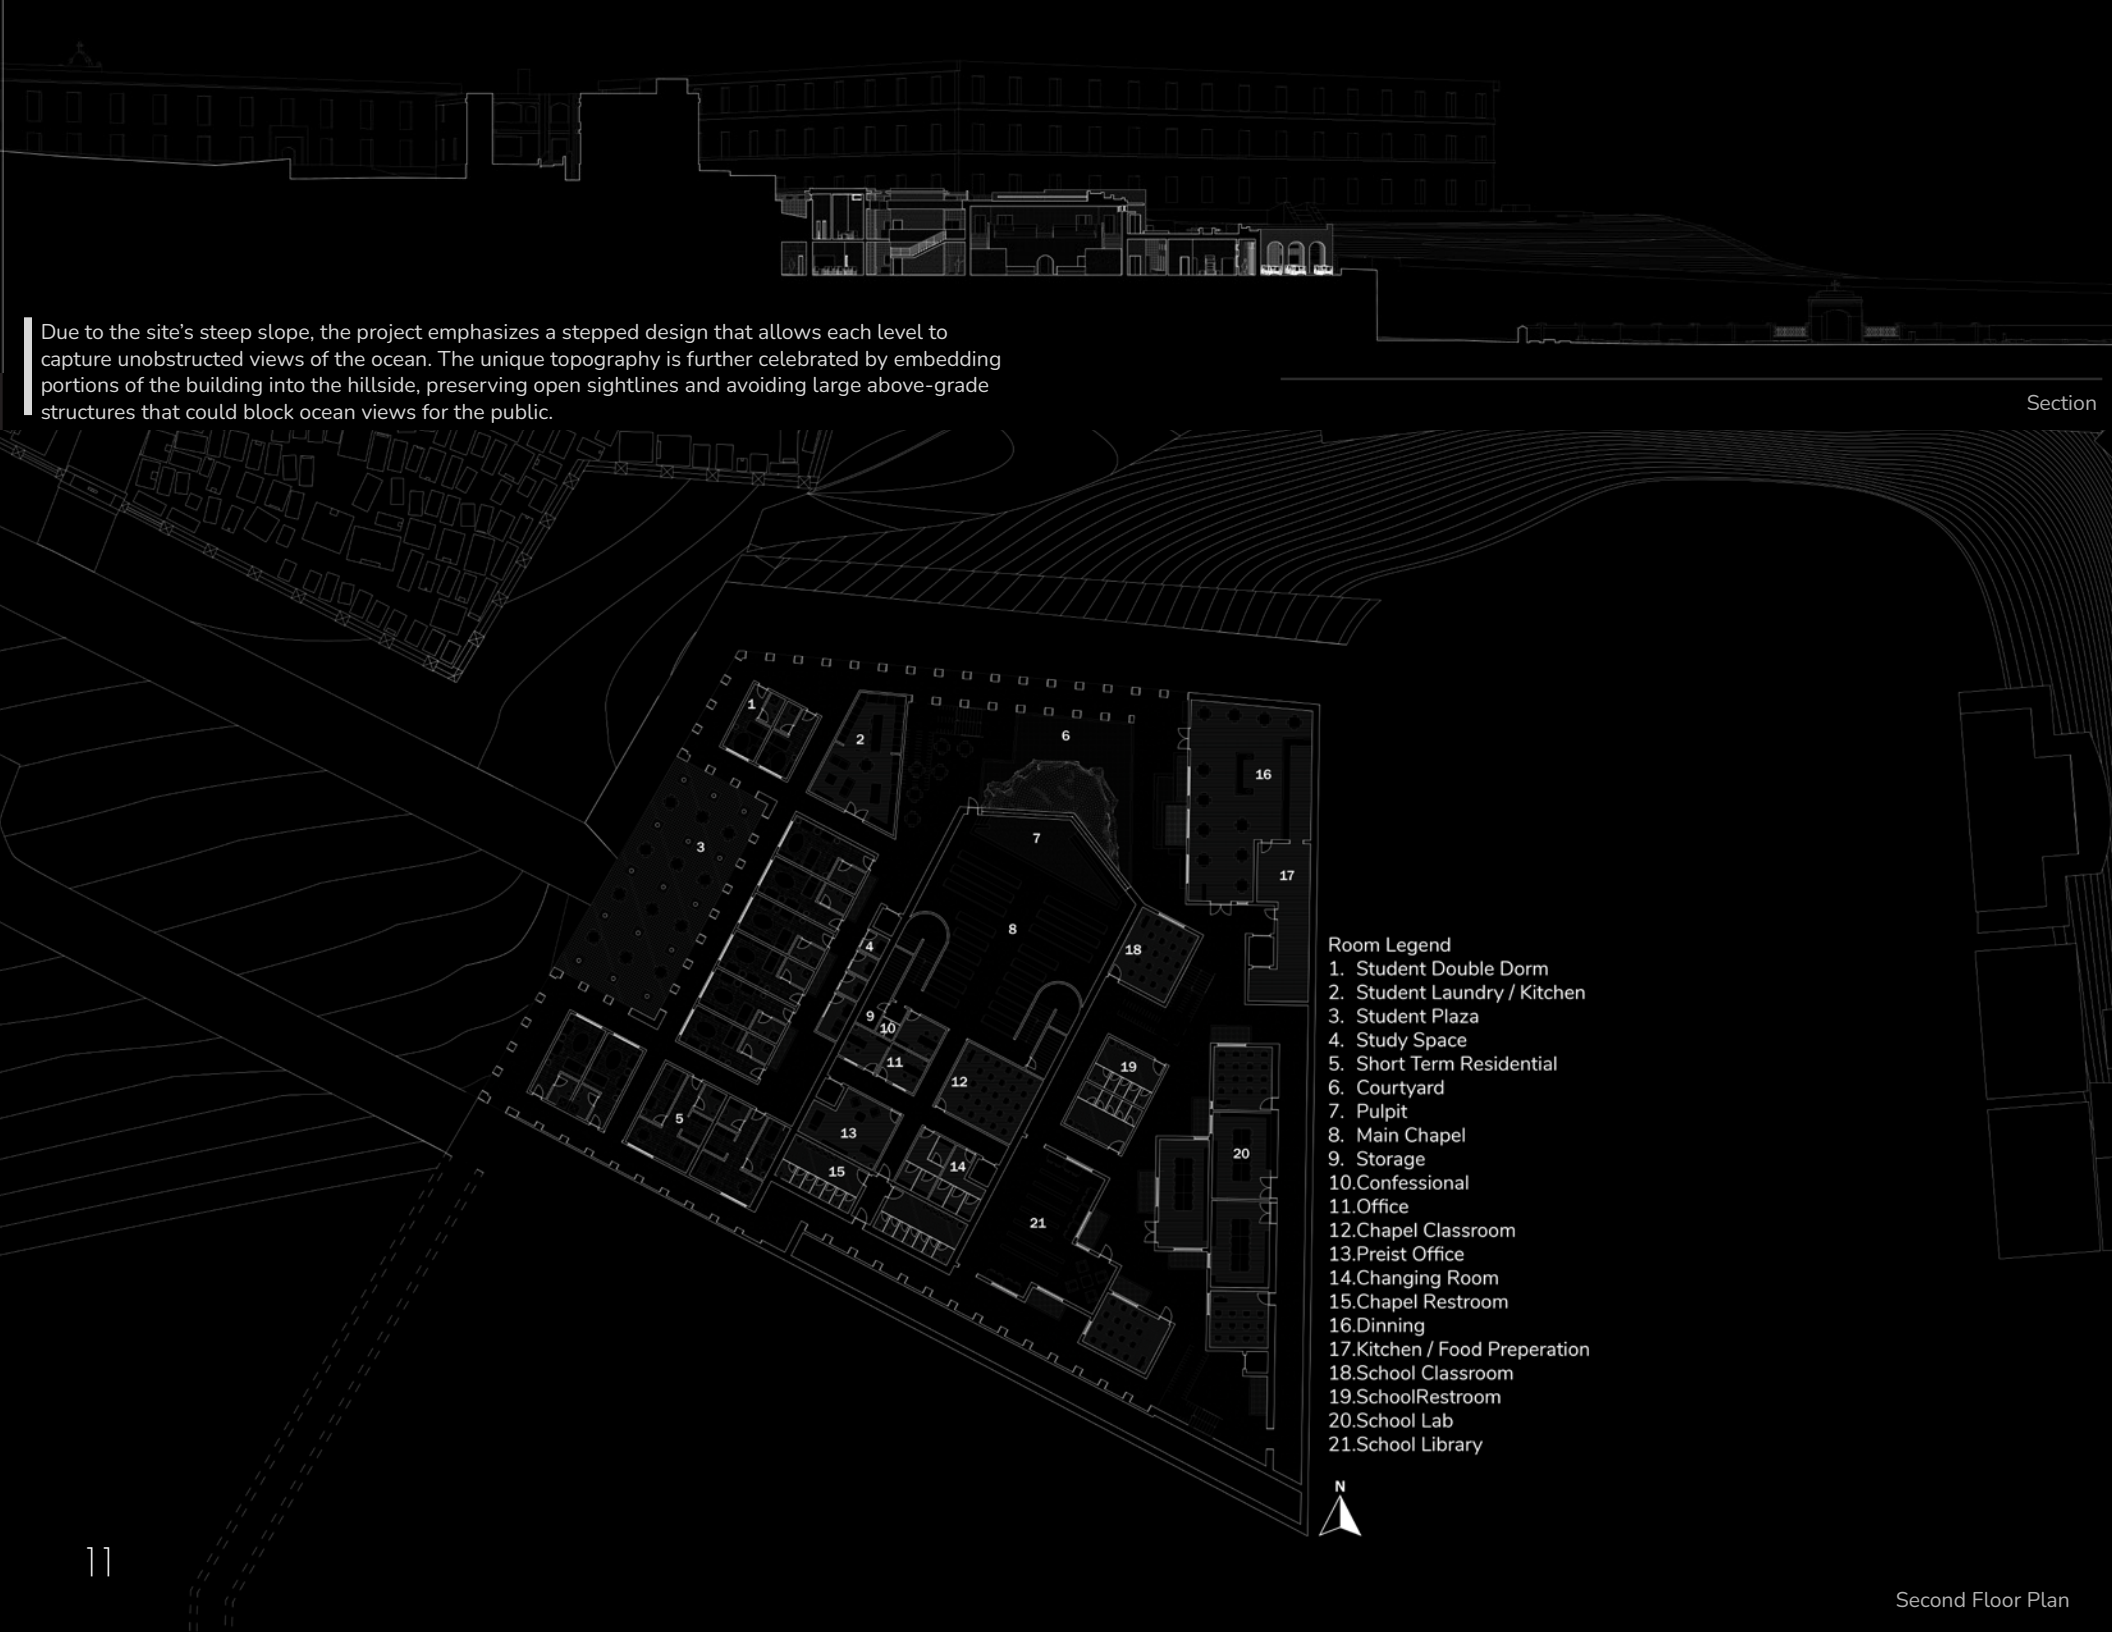



# 03 Penetrate

Techniques:  
Photoshop  
Rhino  
Lumion

Project Penetrate focuses on the **landscape of the site** and how the site can introduce the architecture.

Roof Plan

The studio class is inspired by Frank Lloyd Wright's teachings and ideology by considering the site and its **surrounding environments**.

The project contained a "client" who had specific needs for the space, such as an **art studio** and a space to have a **gathering** of small group that can be unrelated to the artist studio and office.

Model Photo

Elevation

Model Photo

Model Photo

Model Photo

Model Photo

The architecture splits the space with a rammed earth wall that **extrudes** from the ground separating the two functions of space while allowing the view of the river to be **uninterrupted**.

Floor Plan

Section

Frank Lloyd Wright emphasized the importance of tailoring designs to the needs and **personalities** of his clients. Wright's designs were characterized by a high degree of **customization**, reflecting the **individuality** of the occupants and their lifestyles.

Section




# Invigorate

Techniques:  
Hand Drawing  
Layering  
Physical Model Building  
Photography  
Photoshop

Lighting Study Photo

The Florida landscape is unique with its flooded, flat landscape. The design intent of the Florida Landscape project is to create a structure that could **manipulate** and **accentuate** the perks of the flooded landscape. The project houses a bath house that would accommodate individual and group baths. The main inspiration of the project was a traditional Japanese bath house. The research on Japanese bath houses introduced rituals and chores that the individuals would perform prior to bathing.

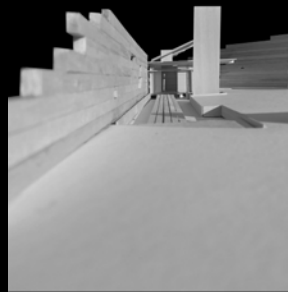

Entrance Model Photo



Exterior Entrance Perspective

The material palette would contain rammed earth and concrete to assist with the hot climate of Florida. The project **manipulates** the water and sunlight to create a **harmonious** experience to the individual. The plan was to create an **invigorating** and **celebrated** space that continues beyond the confines of solid land and spans across the water.

The inhabitant would walk above the water and be able to touch the rammed earth upon entering the bath house. Entering the space, a genkan step invites the individual to remove their outside footwear which creates a moment of **pause** before entering the main space.



Diagrammatic Map Plans

The form of the bath house was created by finding the winter solstice line and creating an **axis** the project would revolve around.




Main Space Interior Perspective

The rammed earth wall was designed to be placed across the water to create a **seamless** connection between defined and undefined ground. The inspiration came across a fisherman and the limit of his ability to move beyond the defined ground before him. By understanding the limitations, the architecture can stitch the fine line between ground and water.



Site Diagram

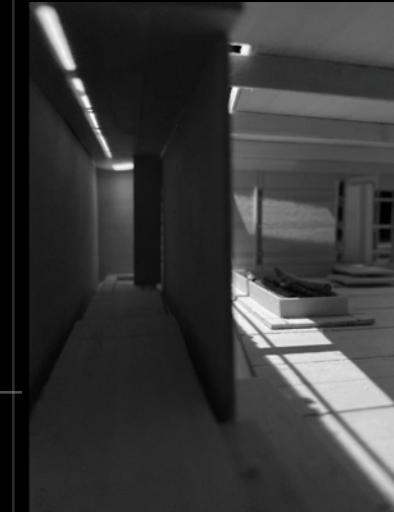

Interior Model Photo

The **reflection** space that is tucked between the wall and furnace creates a dark space that emits small **slivers of light** to penetrate the space and create moments of **reflection** across the ground.

The rammed earth wall **splits** the main space into two spaces: **private** and **public**. On the public side, the space contains the group bath and light **reflection** space. The water is heated by a wood burn furnace. The water is then dispersed onto the bath locations initially upon entering the baths.

Drawn Floor Plan



Model Photo

